

EX 3.3 | LIBERTY GARDENS

CAMILA MEZA


ARCH 196

PETROCELLI

SPRING 2023

DESIGN STATEMENT + PROGRAM DESCRIPTION

LIBERTY STATE PARK IS AN ATTRACTION FOR VISITORS AND TOURISTS FROM ALL OVER THE WORLD. FROM THIS VAST PARK THE SKYLINE OF NYC AND THE STATUE OF LIBERTY ARE PROMINENTLY SHOWN. THE EXISTING ADMINISTRATION BUILDING AND ROUNDABOUT DOES NOT HIGHLIGHT THE SITE WELL. THE OLD BUILDING TAKES AWAY FROM THE SITE, IT DOESN'T DO MUCH OTHER THAN IT'S SOLE PURPOSE AS A STANDING STRUCTURE. VISITORS ARE ARRIVING AT THE PARK WITH HIGH EXPECTATIONS, SO THOSE EXPECTATIONS SHOULD BE MET. THE GOAL OF THE DESIGN IS TO USE NATURE AS A SETTING TO CREATE A STYLIZED URBAN PARK. VISITORS CAN ENJOY NATURE AND INTERACT WITH IT. THE DESIGN IS A CONCEPTUAL PARK, WHICH INCLUDES THE MAPLE TREES AND ROCKS. THE LOCATION OF THE BUILDING IS WHERE THE TREES ARE BECAUSE THE BUILDING SHOULDN'T INTERRUPT OR BLOCK VISITORS, SO IT'S BEING MOVED INTO THE TREES WHERE A SENSE OF PROTECTION IS GIVEN. THE MODULES ARE SMALLER, REPEATED AND SPREAD OUT AROUND THE TREE AREA. THESE MODULES ARE A COMBINATION OF PLAYGROUND/JUNGLE GYM, DAYCARE, AND ADMINISTRATION OFFICES. THE PLACEMENTS OF THE STRUCTURES AND THEIR PURPOSE HAVE BEEN PLACED BY THE CONSIDERATION OF SOLAR ORIENTATION. HAVING THE OFFICES FACING NORTHEAST WILL BENEFIT THE OFFICE SPACES WHEN THE SUN IS RISING. SOME STRUCTURES WILL BE LEFT OPEN AND SOME WILL BE CLOSED FOR OFFICE SPACES. ONE OR TWO STRUCTURES WILL HAVE AN OPENING APER-

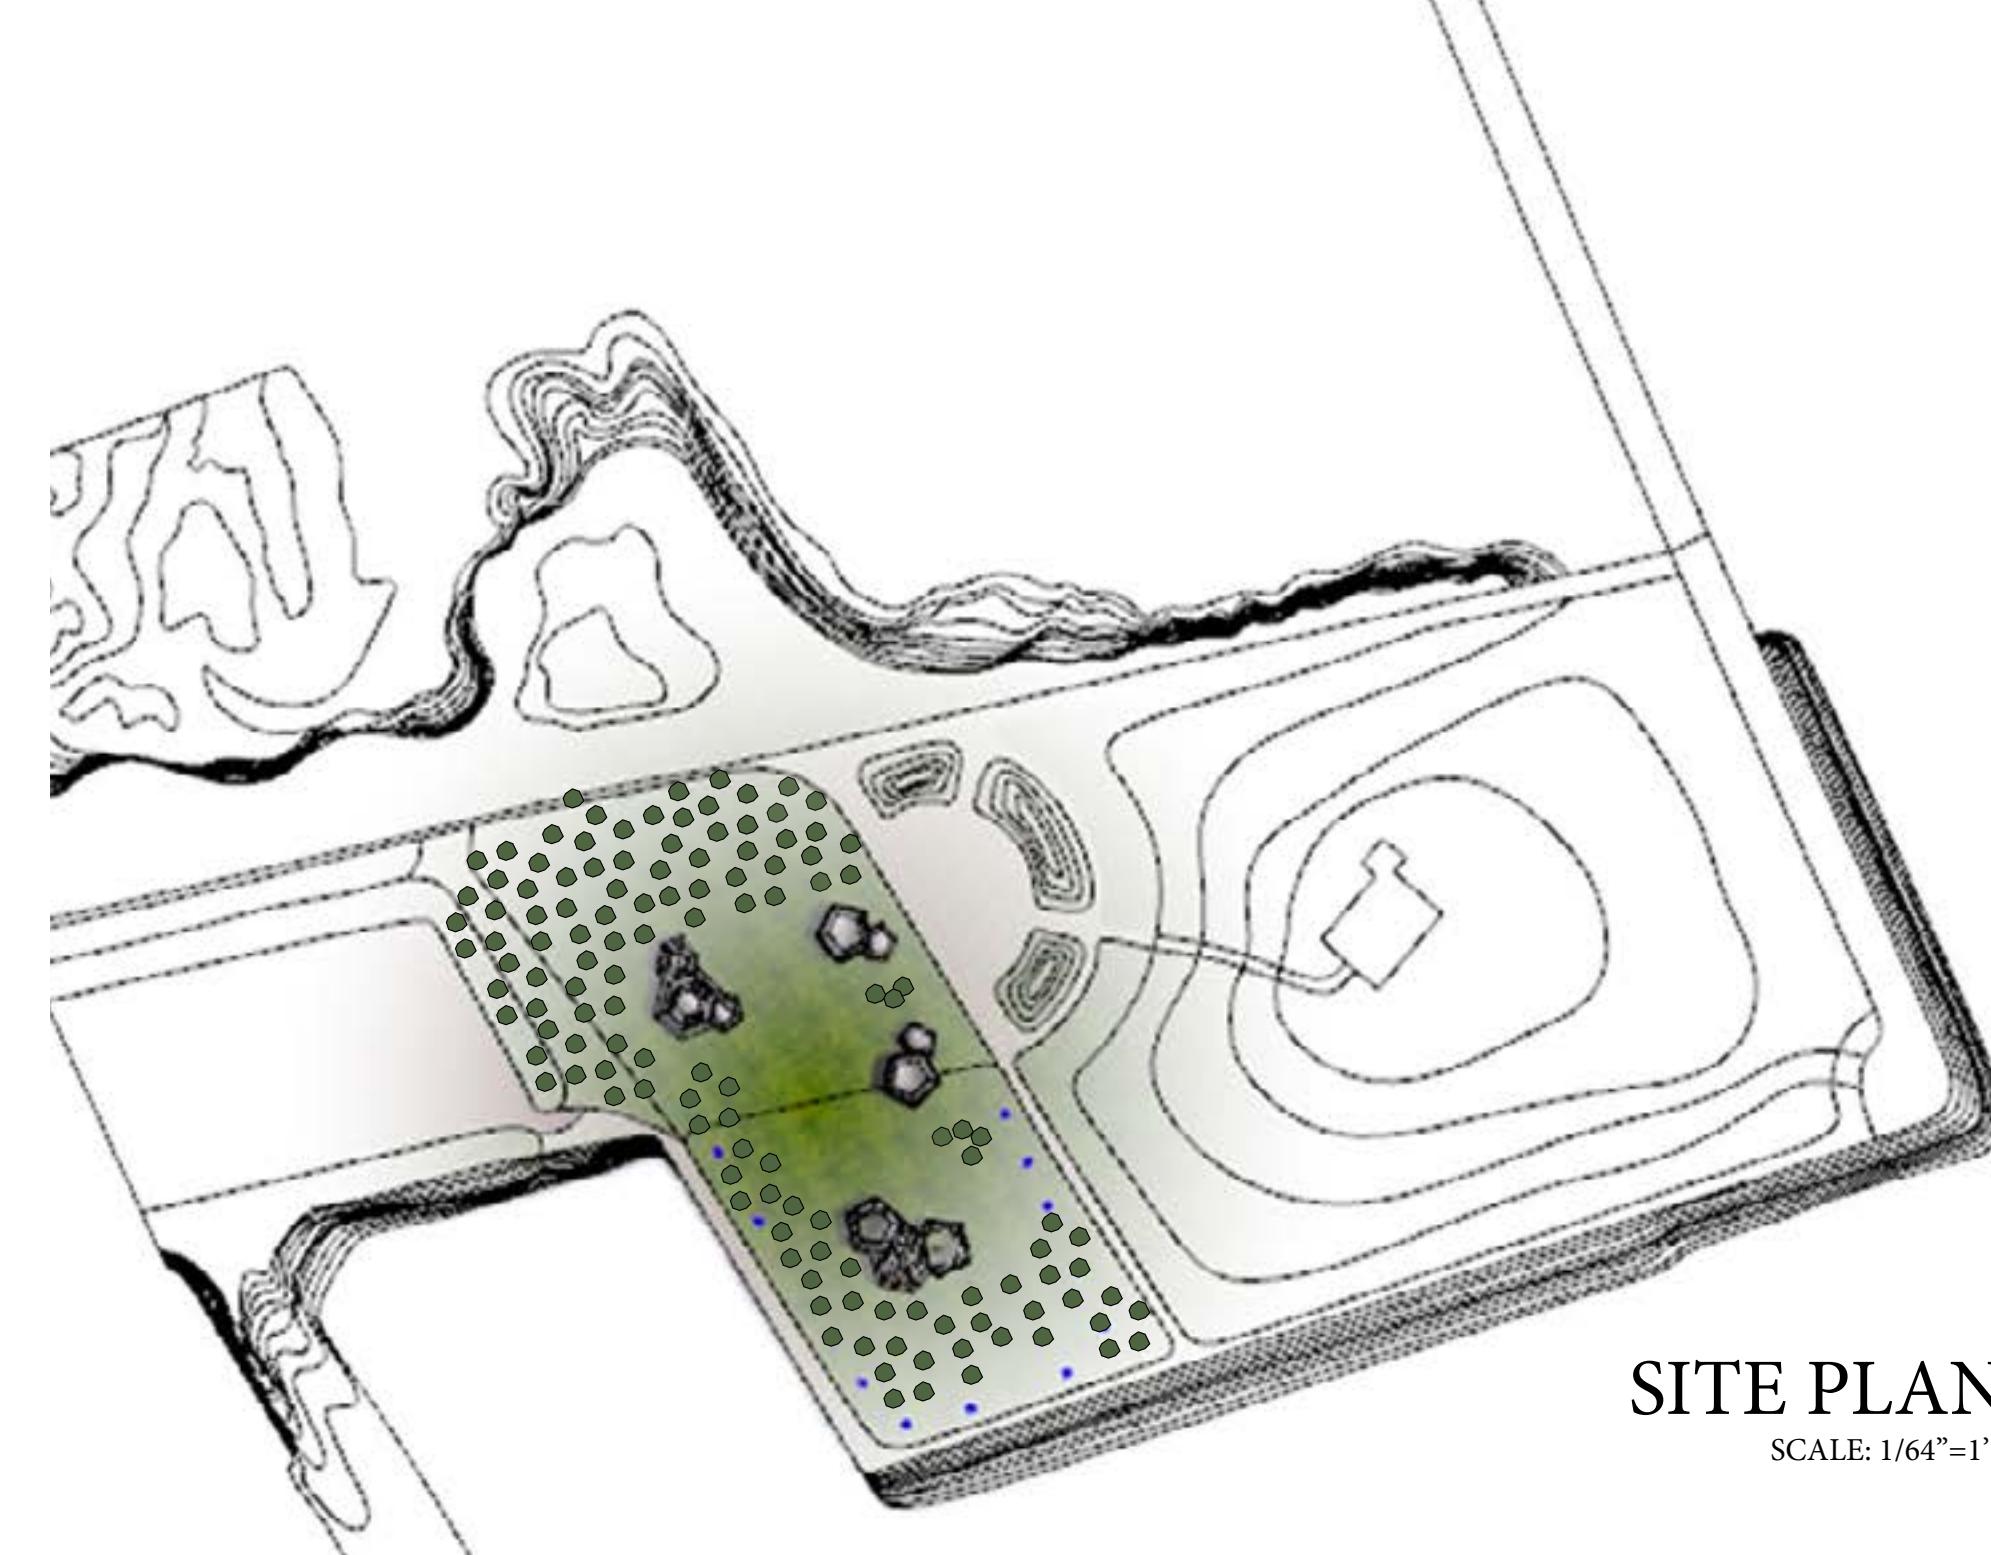

SITE PLAN



Bristol Gaming Dome




MinYaoli Luxury Tent Hotel, China





The Benton House, Colorado
architect: Charles Haertling
Known as a 'weird house' with pods that contain the main living areas. The exterior is monolithic and a type of heavy organix material.




PROCESS+CONCEPT

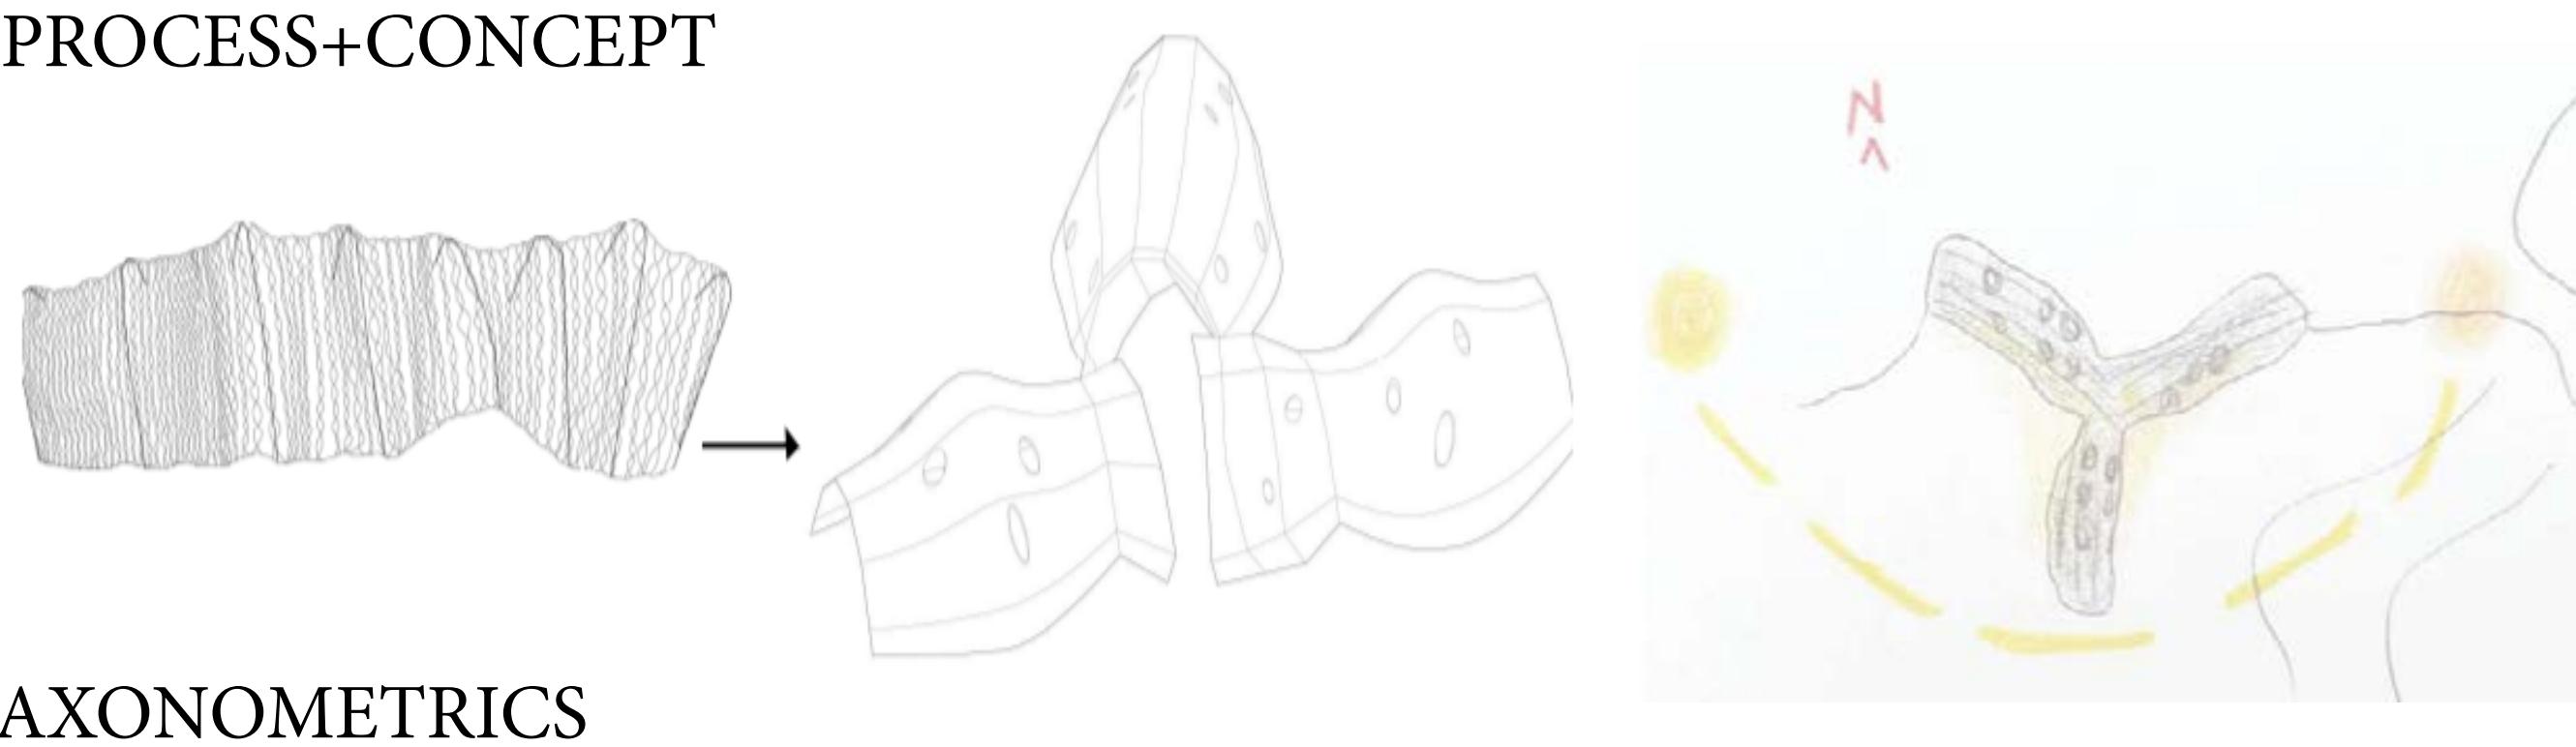

AXONOMETRICS

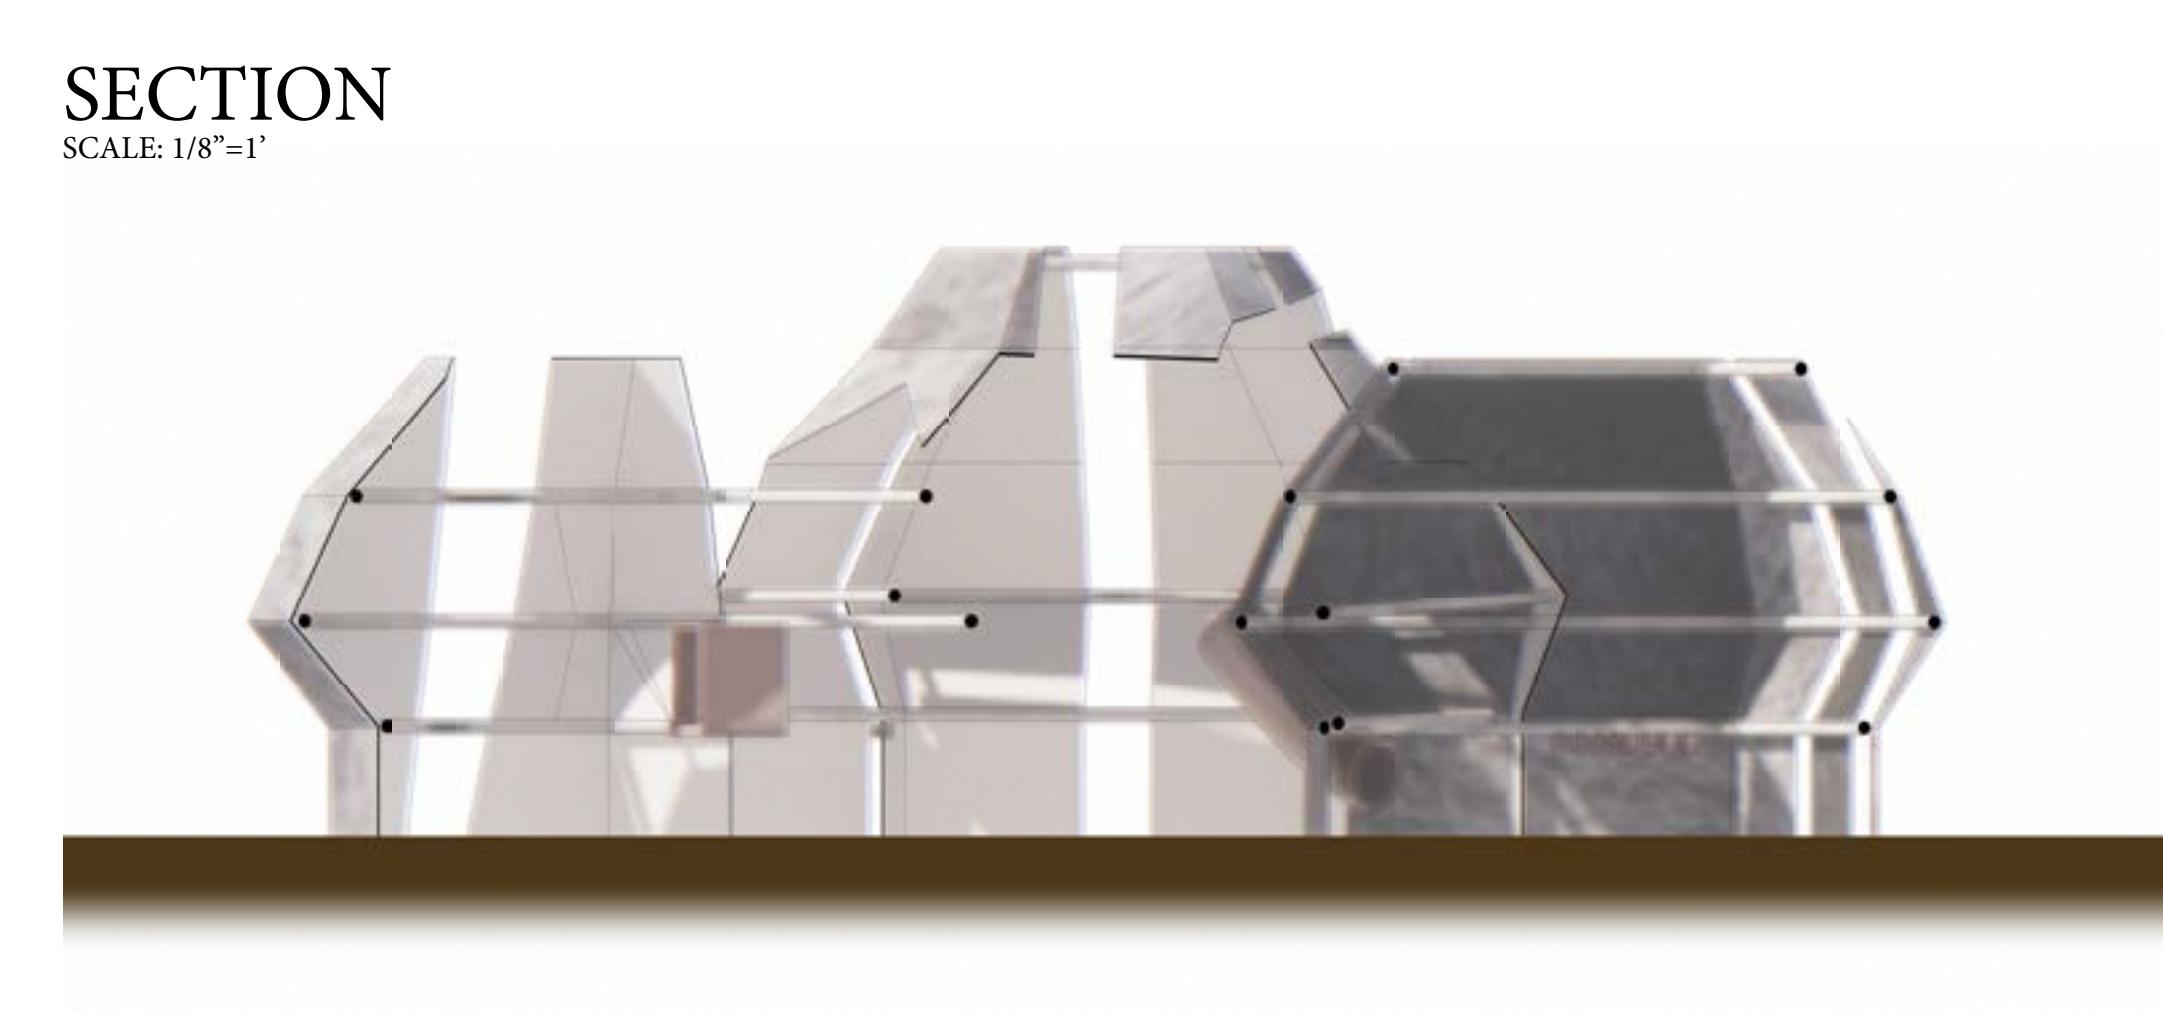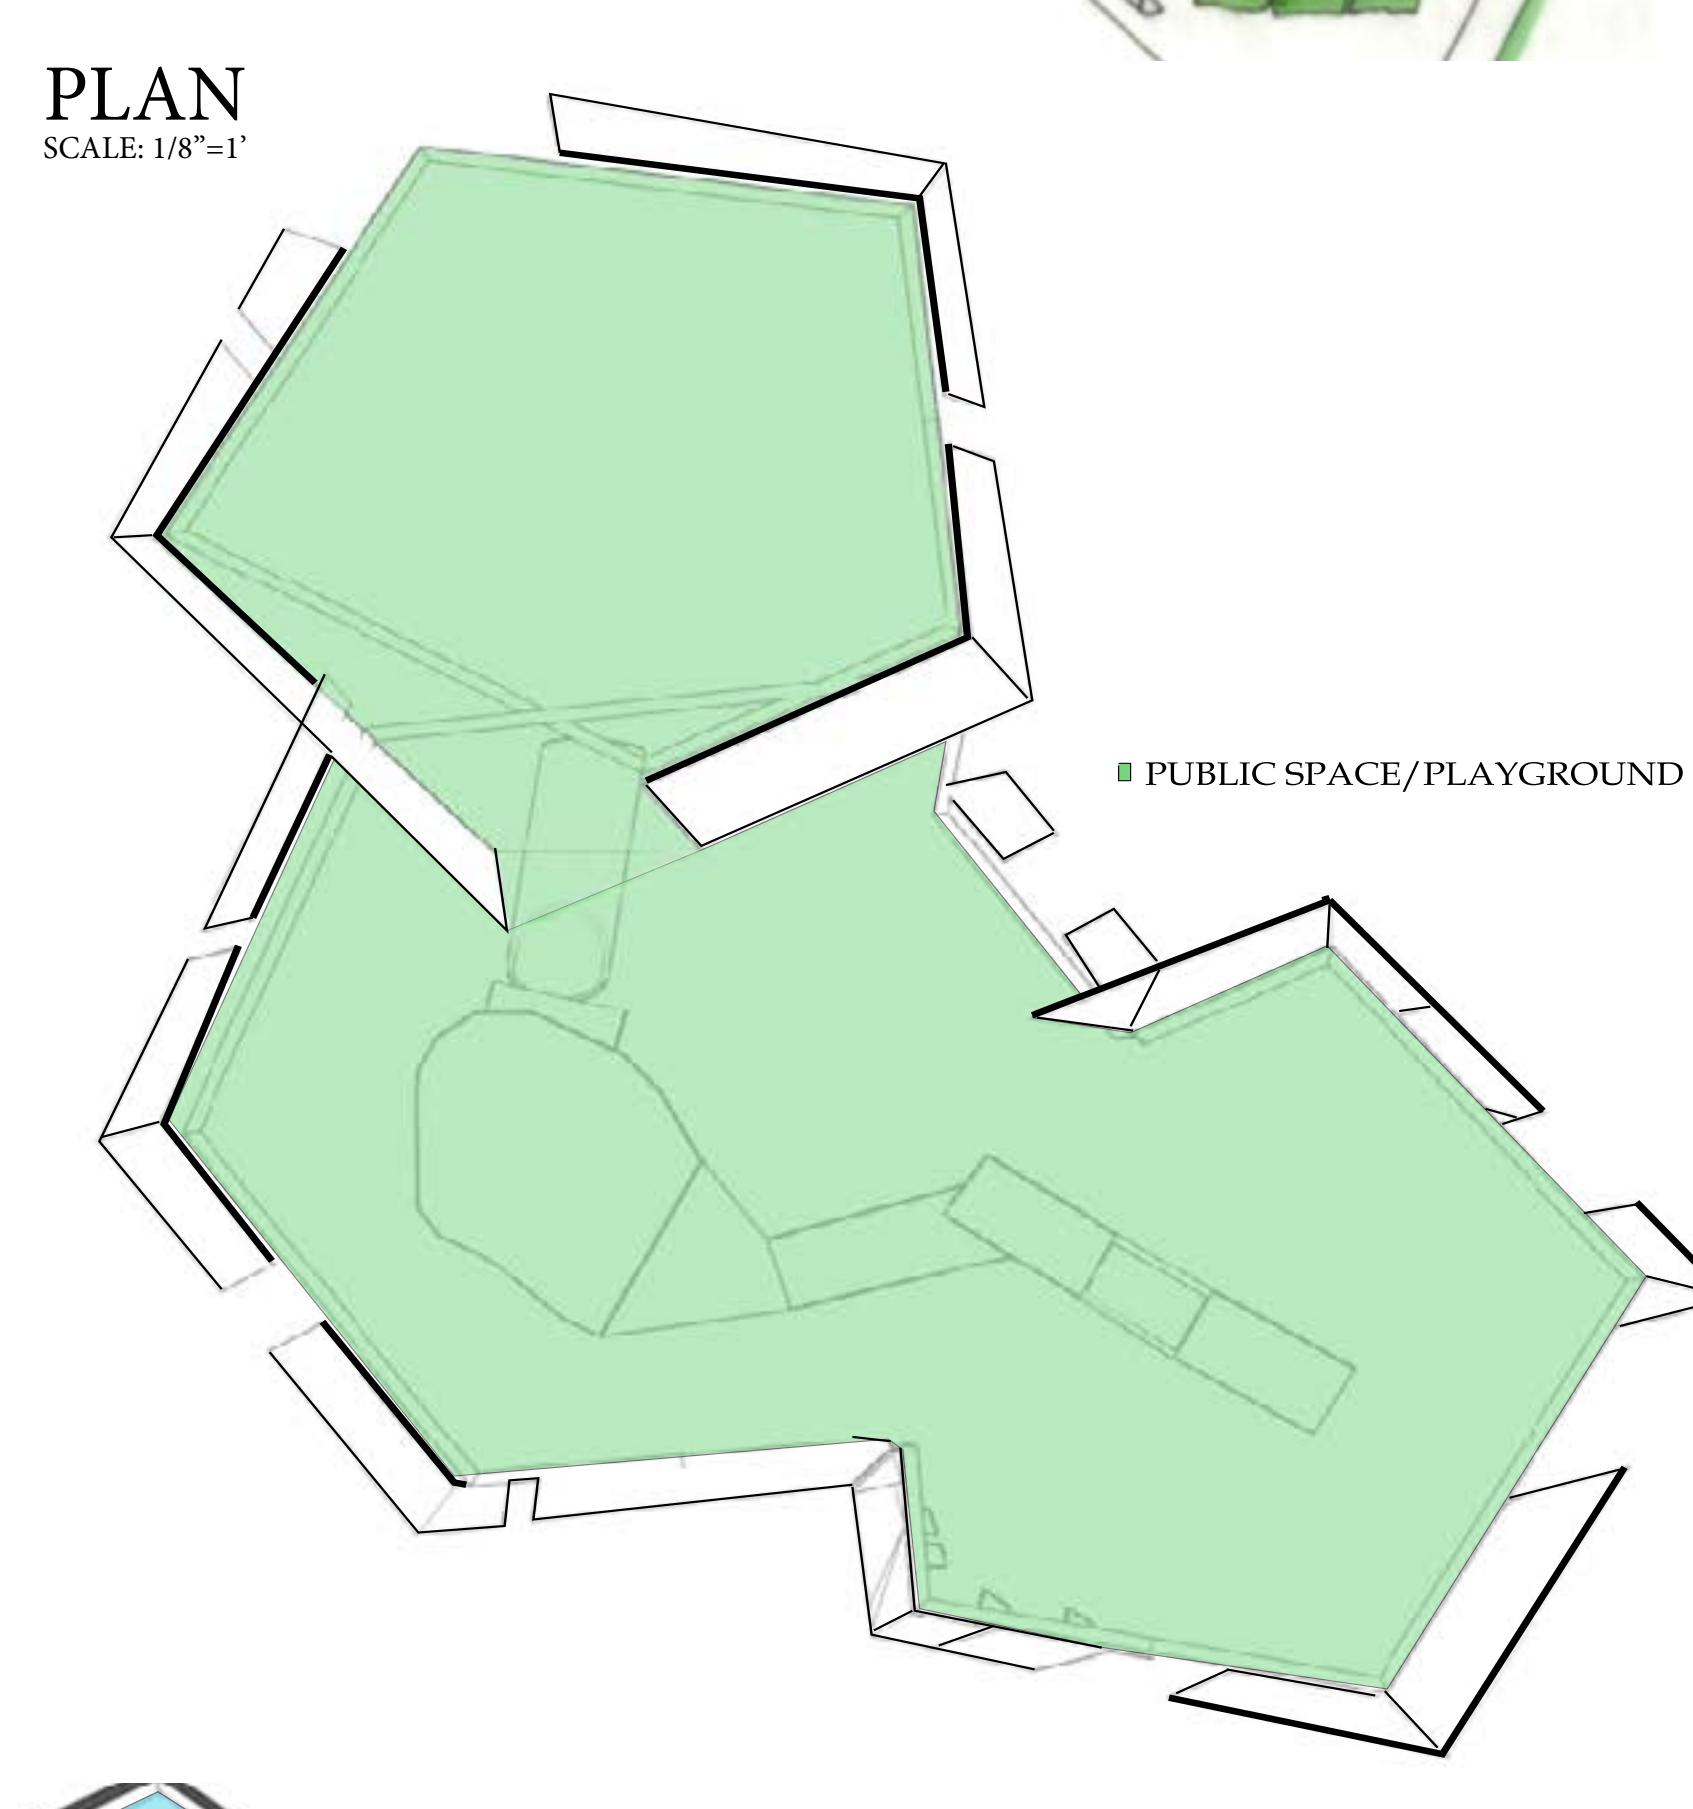

EXPLODED AXONOMETRIC

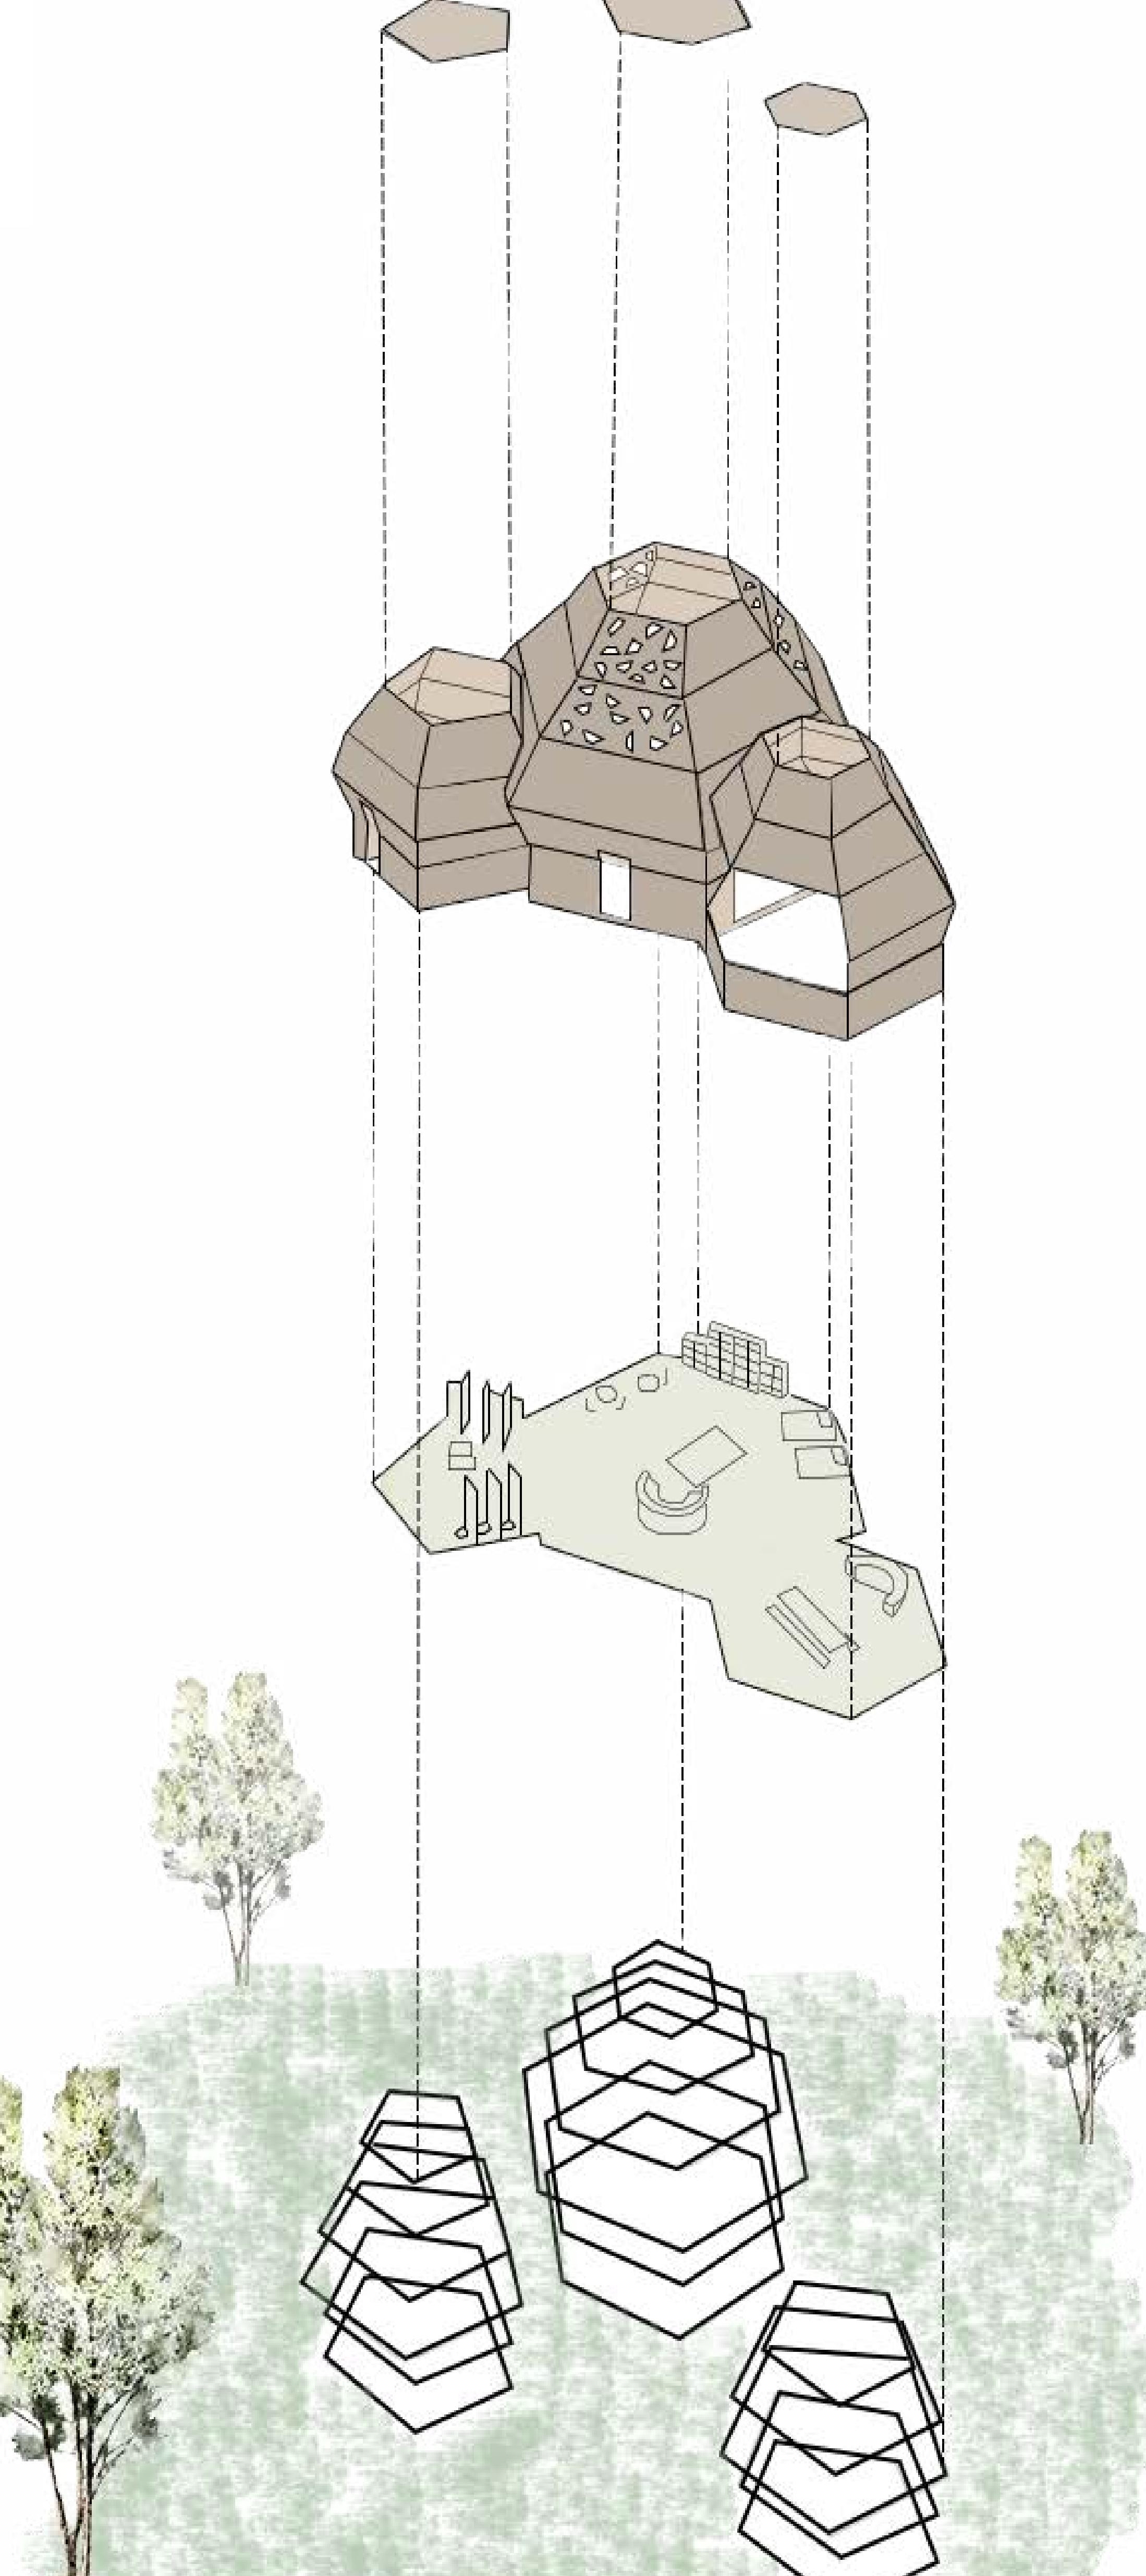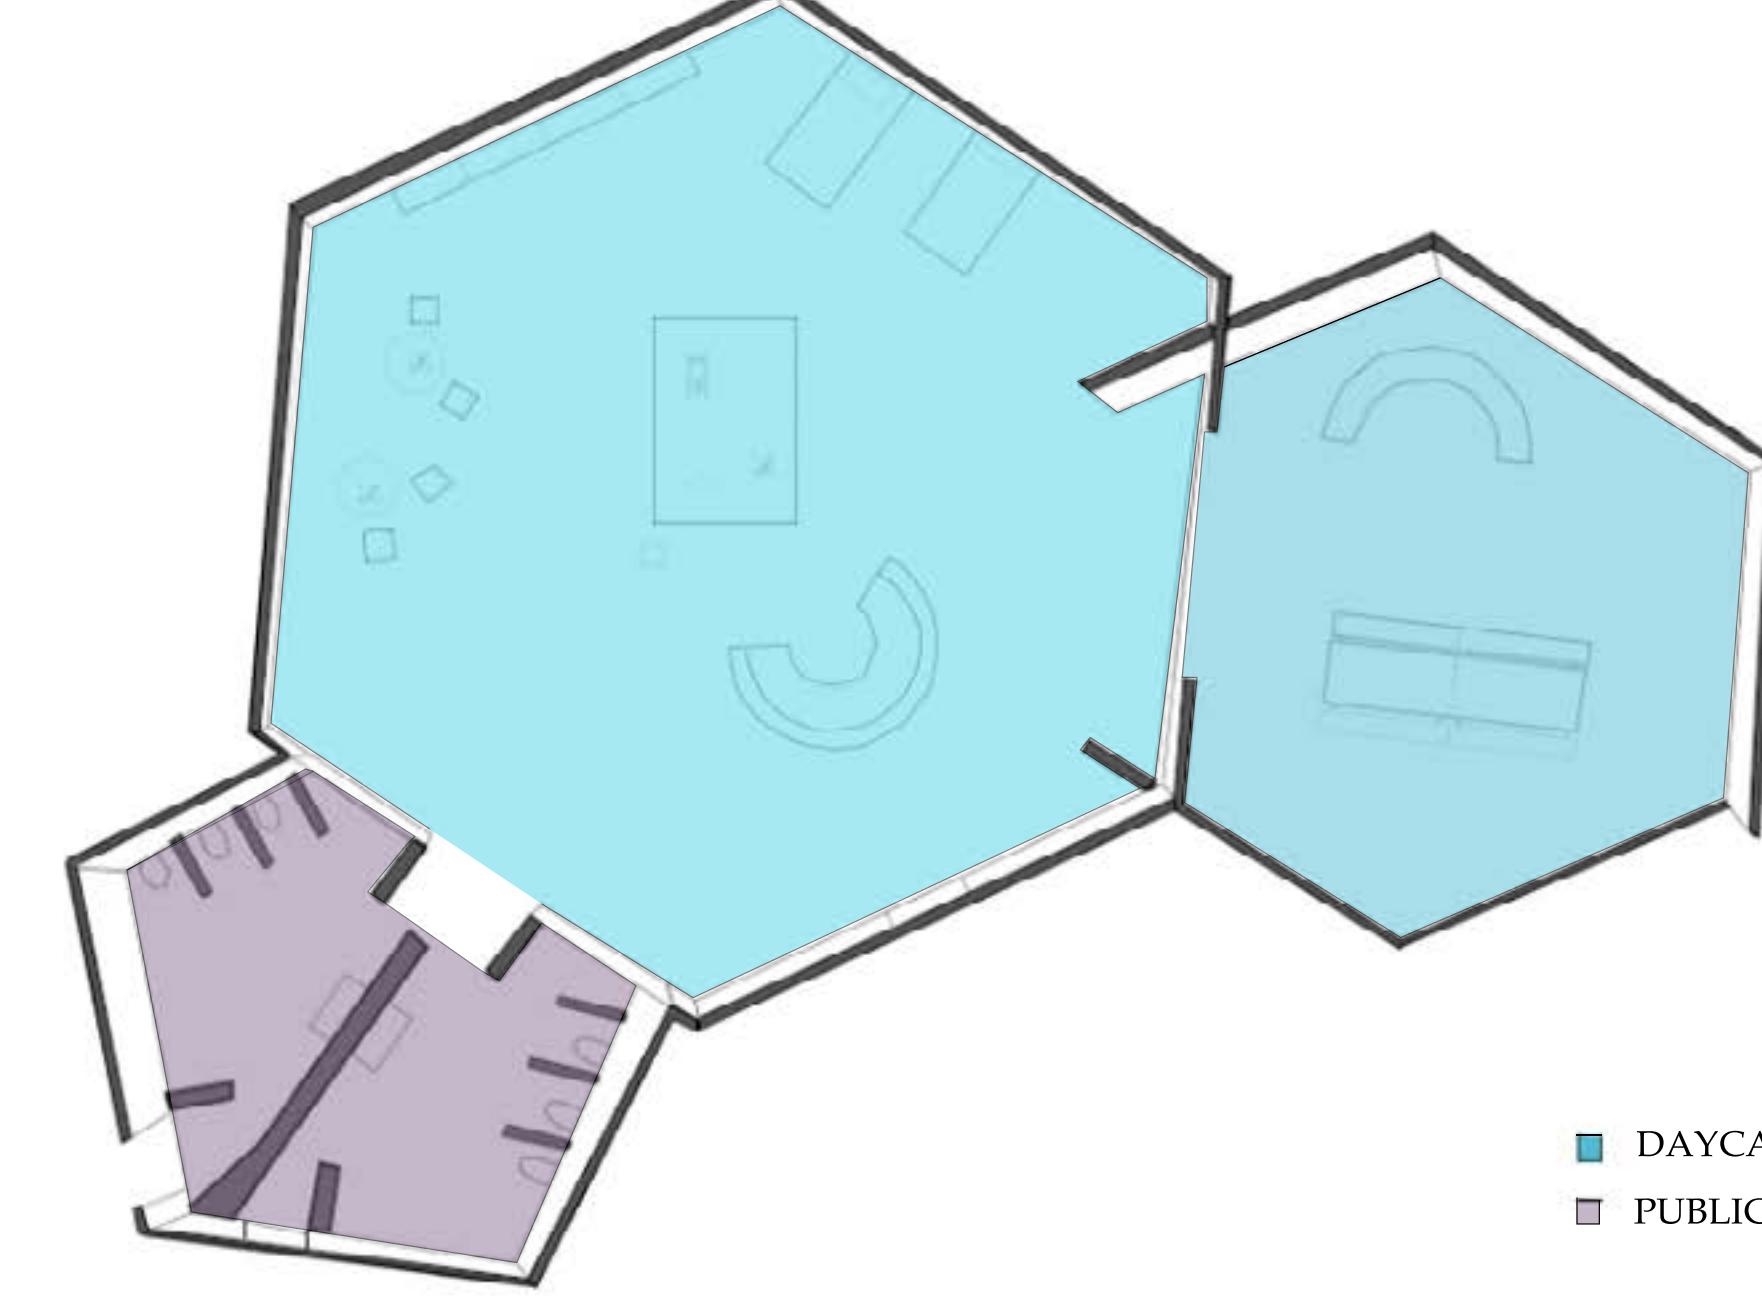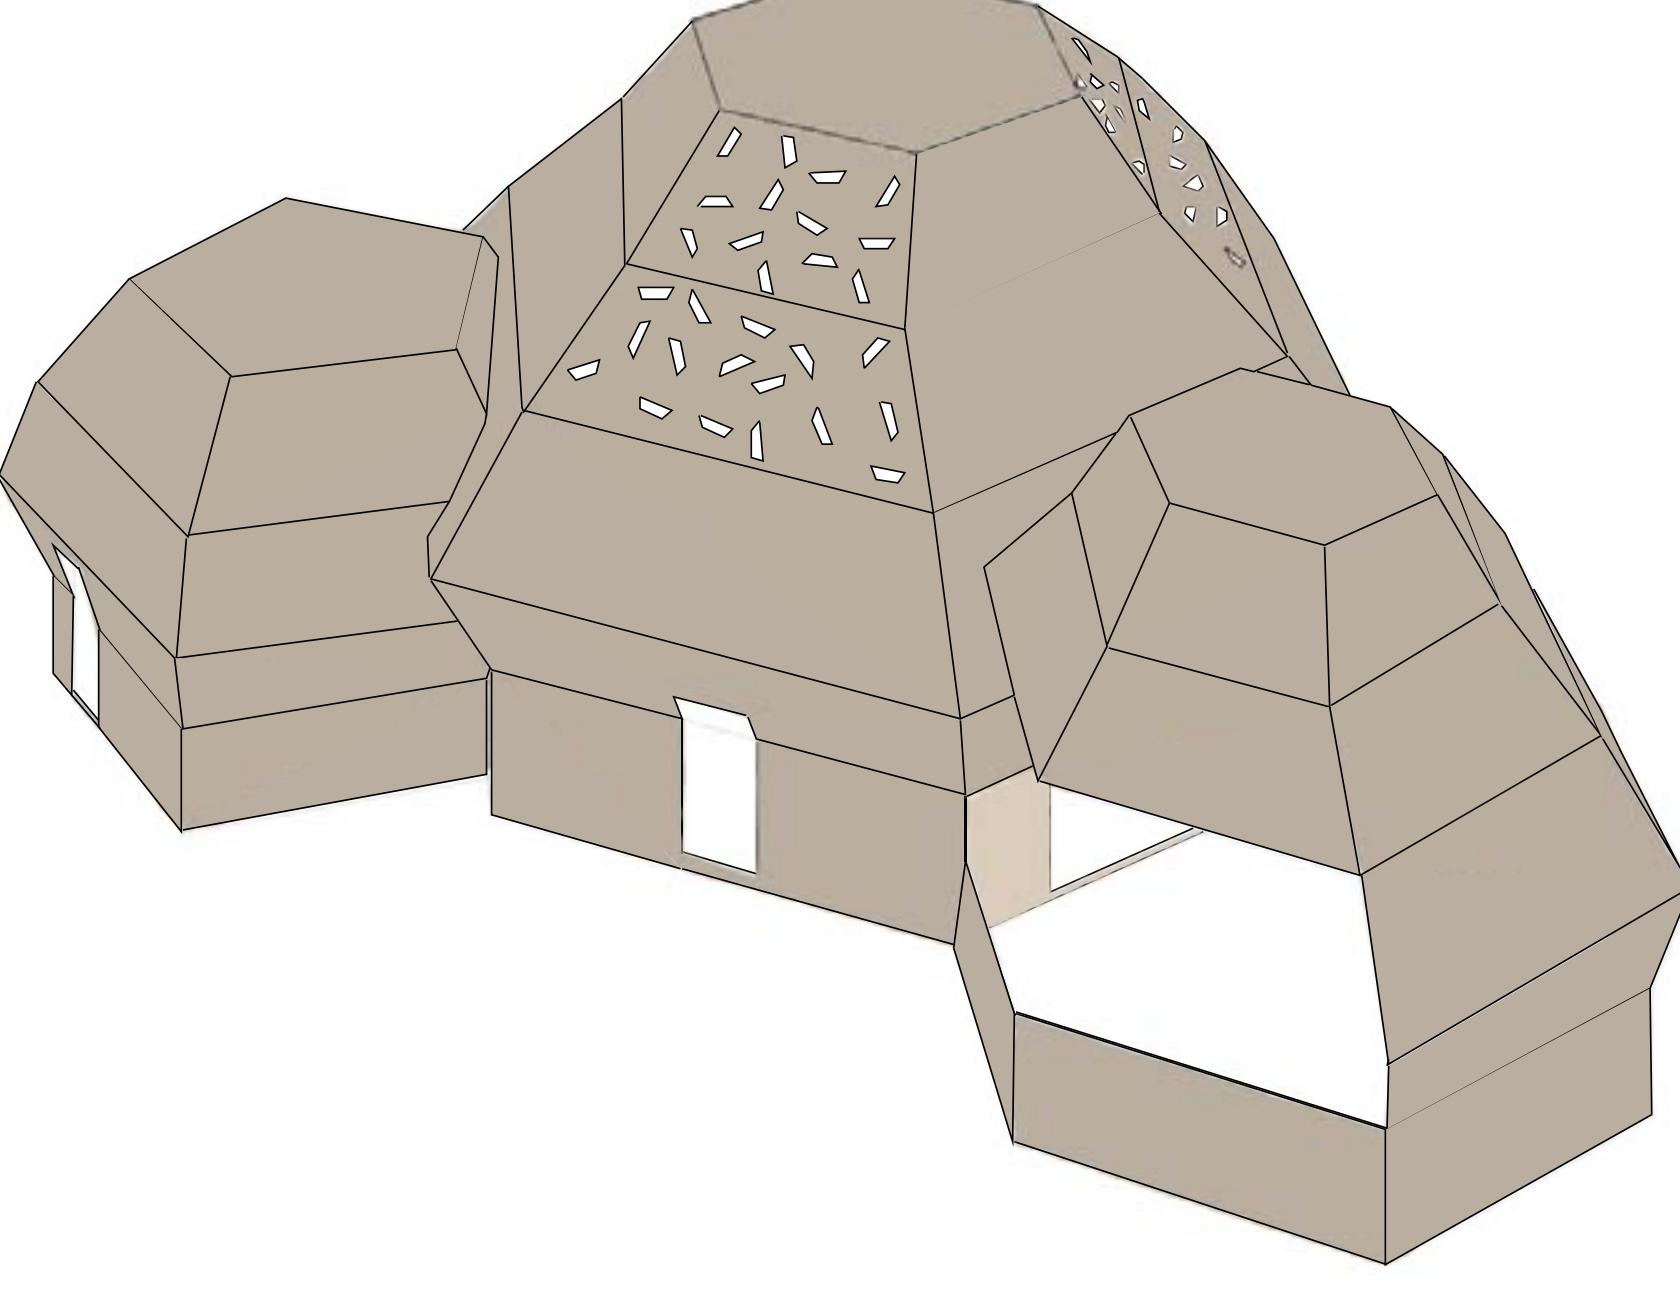

PERSPECTIVES



ELEVATION

